


ÜBERBAUUNG MAIENHOLZ, MAIENHOLZ 15, 5018 ERLINSBACH, PARZ.- NR. 1068

FARB- und MATERIALKONZEPT
AUSFÜHRUNG

objektnr. / plannr.	130 / 130.500.1	erstellt am:	27.06.2025
massstab:		geändert am:	25.08.2025 bk/mk/lw / Index D
plangrösse:	A2 (42 / 59.4cm)	ausgedruckt am:	22.01.2026
FIXPUNKT 4418 = 473.378 M.Ü.M		S:\130_Überbauung Maienholz Erlinsbach	
± 0.00 B FER EG REFH A & B = 468.50 M.Ü.M		\07_Vermarktung\130_Überbauung Maienholz_ac27	
		Vermarktung.pin	
Stritengässli 24	5000 Aarau	Telefon 062 825 27 27	info@architektengruppe.ch www.architektengruppe.ch

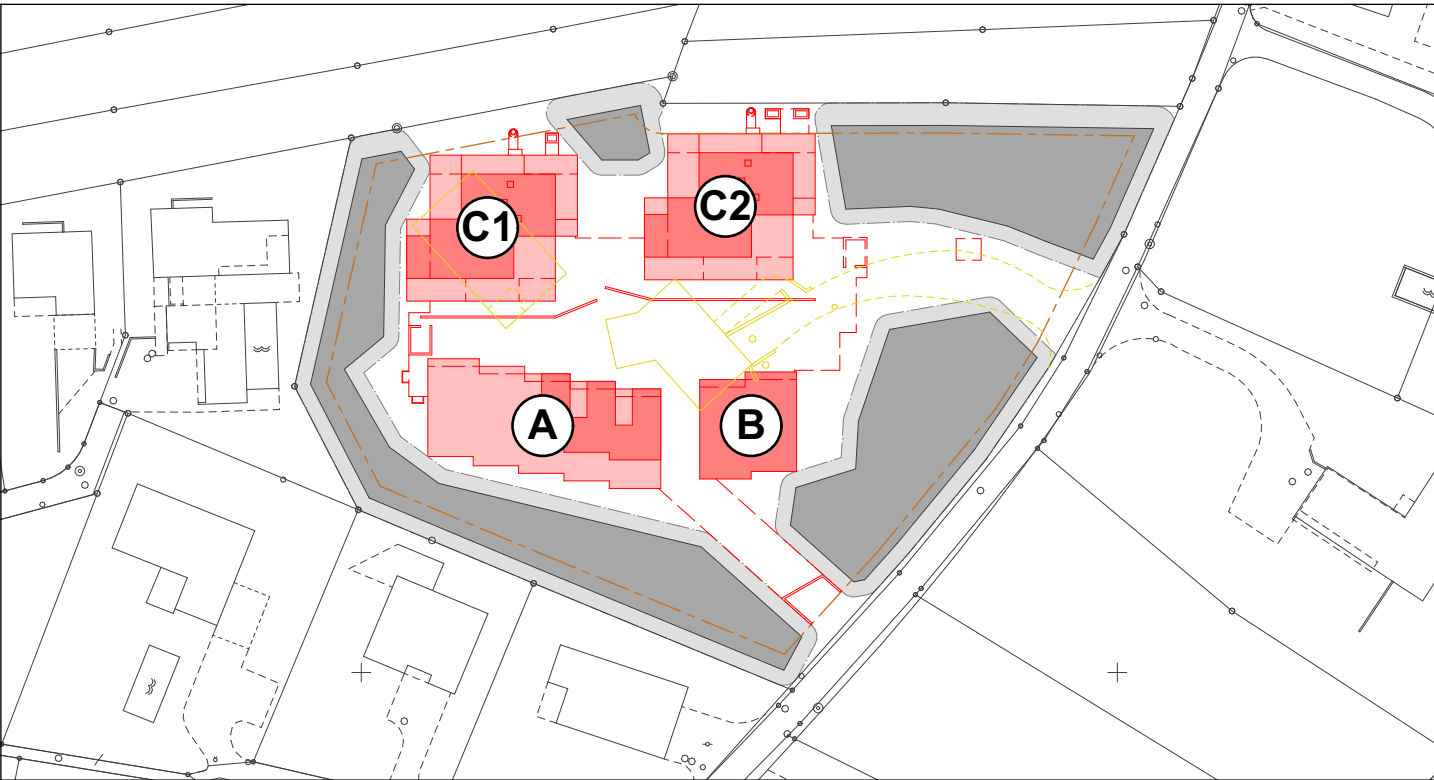

	beton	AK	aussenkant	K	kurbel	INST	installationsschacht
	sichtbeton	OK	oberkant	M	motor/ elektroantrieb	SAV	sanitärverteilung
	backstein	UKD	unterkant	VR 90	verbund- raffstore	BHV	bodenheizungsverteilung
	kalksandstein	b roh	oberkant boden roh	MFB	metallfensterbank	ELV	elektroverteilung
	betonfertigelemente	b fer	oberkant boden fertig	DK	drehkipplügel		
	dämmstoffe	m.ü.m.	meter über meer	KS	kühlschrank	KR	kabelschutzrohr
	holzwerkstoff	st roh	unterkant sturz roh	BO	backofen	BA	bodenablauf
	B / MB therm. getrennt	st fer	unterkant sturz fertig	MW	mikrowelle	DW	dachwasser
		sw	schwellehöhe	ST	steamer	fstr	fallstrang
		br	brüstungshöhe	GS	geschirrspüler	stg	sturzgefälle
		DILA	dilatation	WM	waschmaschine	spst	spülstützen
		LS	lichtschacht	TU	tumbler	ES	einstiegschacht
				HTR	handtuchradiator	SS	schlammsammler
						WAS	schmutzabwasser
						WAS-H	häusliches schmutzabwasser
						WAS-R	regenwasser verschmutzt
						WAR-R	regenwasser rein
						WAR-S	sicker reinwasser

±0.00

OK roh

±0.00

OK fertig

±0.00

OK terrain gewachsen

TS

türschliesser

brandschutztüre mit zulassung

EI30

wasserlöschposten

handfeuerlöscher

WLP

handfeuerlöscher

rauchwärmeabzug

HFL

rauchwärmeabzug

RWA

alle masse sind rohmasse und vom unternehmer am bau zu kontrollieren.
innere türhöhen bezeichnen die höhe ab boden fertig, bzw. OK schwelle bis UK sturz roh.

Farb- und Materialkonzept

Hinterlüftete Holzfassade: Holzverkleidung vertikal geschlossen mit Nut und Kamm unterschiedliche Lattenbreiten 95mm, 120mm & 145mm unterschiedliche Lattenlängen 3'000mm, 4'000mm & 5'000mm Farbbehandlung 2-fach maschinell mit Zwischenschliff Farbton deckend und strukturhaltend		dunkelbraun
Balkonuntersichten: Beton gestrichen in:	RAL 9002	Grauweiss
Einstellhalleneinfahrt: Beton, Schalungstyp 2, roh		Betongrau
Treppenaufgänge, Pavillon: Beton, Schalungstyp 2, roh einzelne Wandflächen mit vertikaler Holzverkleidung		Betongrau
Holz-Metallfenster: Aussen: Aluminium einbrennlackiert Feinstruktur, Eisenglimmer, tiefmatt Innen: Holz gestrichen	IGP 5607E77084A30 RAL 9010	Bronze Reinweiss
Sonnenschutz Aussen: Verbundraffstoren (Schenker Storen) Lamellen in Aluminium einbrennlackiert Führungsschienen: Endschiene:	780, Bronze IGP 780, Bronze IGP 780, Bronze IGP	Bronze Bronze Bronze
Stoffstoren vertikal: Gestänge in Aluminium: Textiler Sonnenschutz: Standardkollektion: Schenker Storen AG	eloxiert Sattler 324 024 120	Aluminium farblos Bordeauxrot
Garagentor: Kipptor mit geschlossener Füllung Servicetür mit Streckmetallfüllung Oberfläche einbrennlackiert	IGP 591TE82348R3F	Graubraun
Eingangsfrenten in Metall/Glas: Metall-Glaskonstruktion aus wärmedämmten Verbundprofilen Oberfläche einbrennlackiert	IGP 5607E77084A30	Bronze
Staketengeländer: Flachstahl einbrennlackiert Feinstruktur, Eisenglimmer, tiefmatt	IGP 5607E77084A30	Bronze
Spenglerarbeiten: Dachränder in: Fallrohre in:	- -	Kupfer Kupfer
Briefkastenanlagen: Aluminium einbrennlackiert	IGP 5607E77084A30	Bronze
PV-Module gem. Hersteller Module möglichst reflexionsarm und mit dunklen Rahmen		



130_Süd_Reihenhäuser A



130_Nordost_C1

indexbeschreibung:

A	23.04.2025	Korrektur der Treppendornenaussparungen in den REFH + Ergänzung 4 Dornen bei UG-Antritten (MFH und Aussentreppen) Anpassungen der Deckenaussparungen der Treppe Korrektur und Fertigstellung Kanalisation Ergänzung und Anpassung der Aussenreduitsockel Lichtschacht für Zuluft WP C1 fällt weg; neu Fassadengitter + Winkelemente Ergänzung eines Lüftungskanals in den Schutzräumen Diverse kleine Anpassungen und Ergänzungen
B	27.06.2025	Anpassung der Lichtschächte der REFH WP Ergänzung Elektroanschlüsse der Sonnenstoren Ergänzung Einlage in Deckenstirn bei gedecktem Sitzplatz auf der MFH Attikaterasse Diverse Anpassungen der Fenster
C	09.07.2025 08.08.2025 20.08.2025 21.08.2025 22.08.2025 25.08.2025	REFH A, 1OG, BN-Trennwand Zimmer: Murfor unterste 3 Lagerfugen + Trennlage am Boden upload index C Rampe Einfahrt: Rampengefälle sowie Höhen für Bodenplatte, Wände und Decken korrigiert Nasszellen: Diverse Dusch-WC mit EI-Anschluss (A.3, C1.1, C2.1, C1.201, C2.201) Nasszellen: Diverse Duschentassen mit neuen Abmessungen / veränderte Lage Duschenarmaturen Nasszellen: Wandbelagswechsel konkretisiert
D	25.08.2025	upload index D

